




VAHELAEPLAADI ALUMISE PINNA ARMEERING
1:100

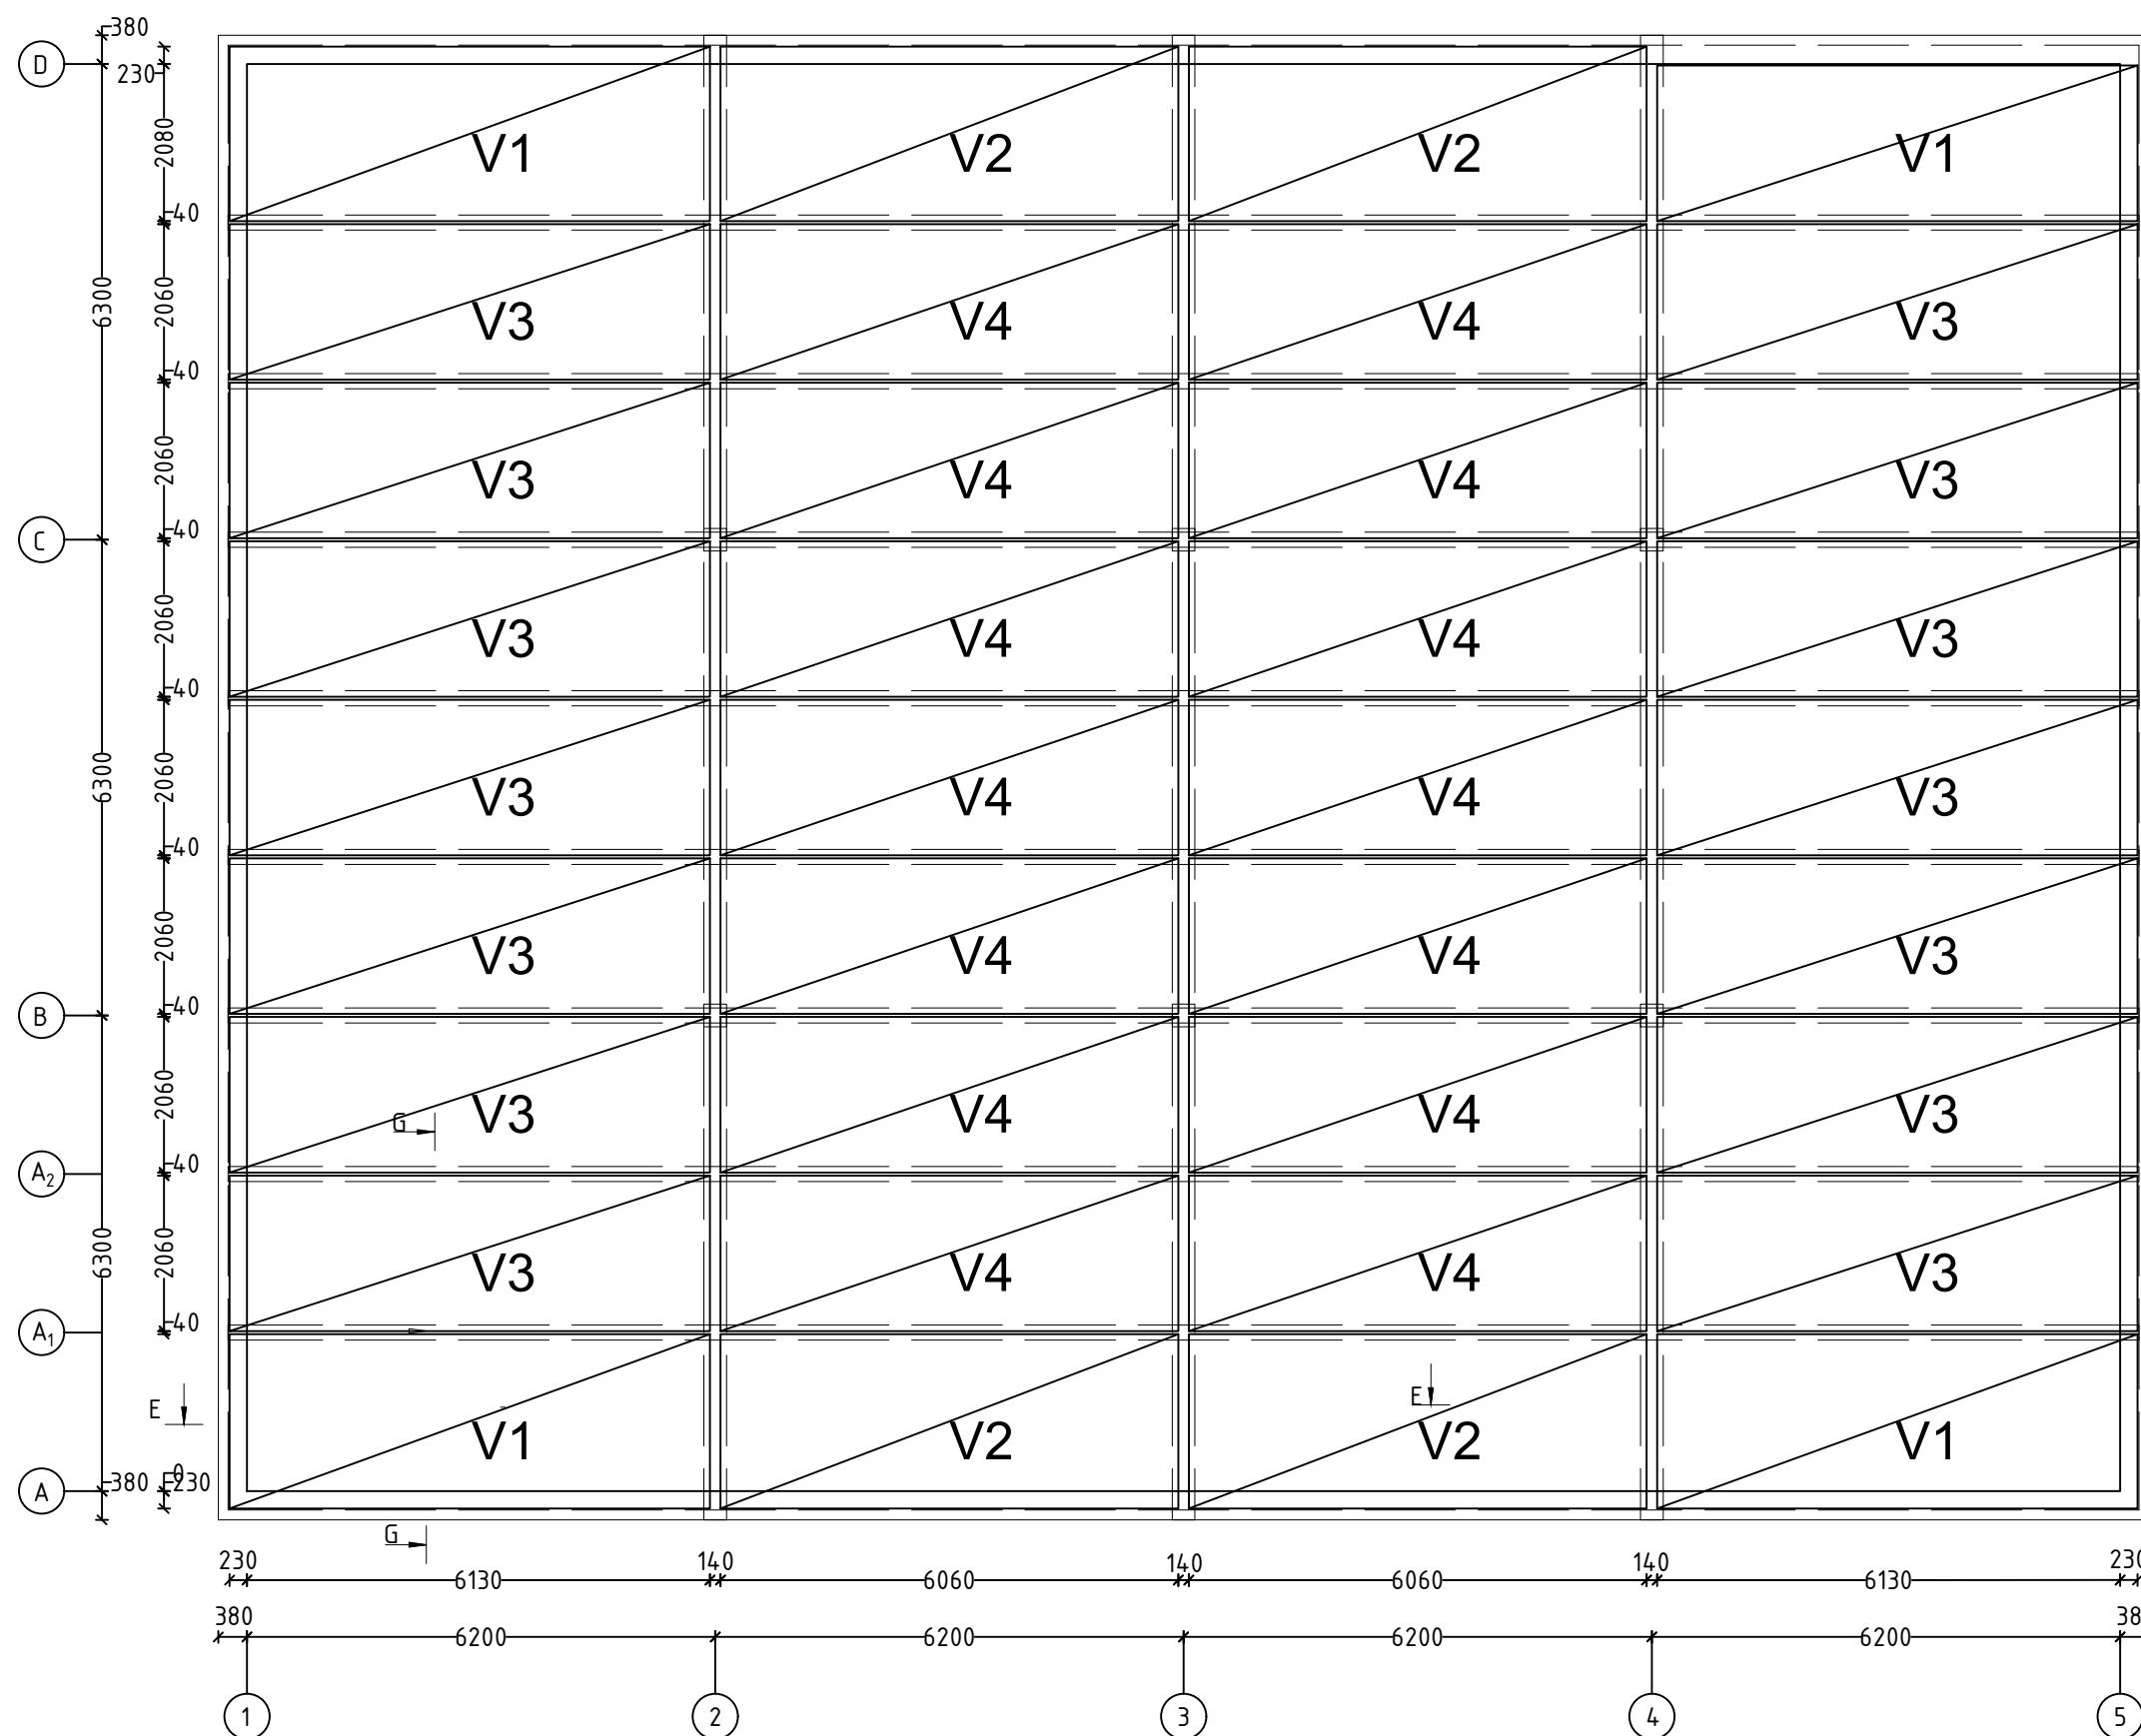



VAHELAEPLAADI ÜLEMISE PINNA ARMEERING
1:100

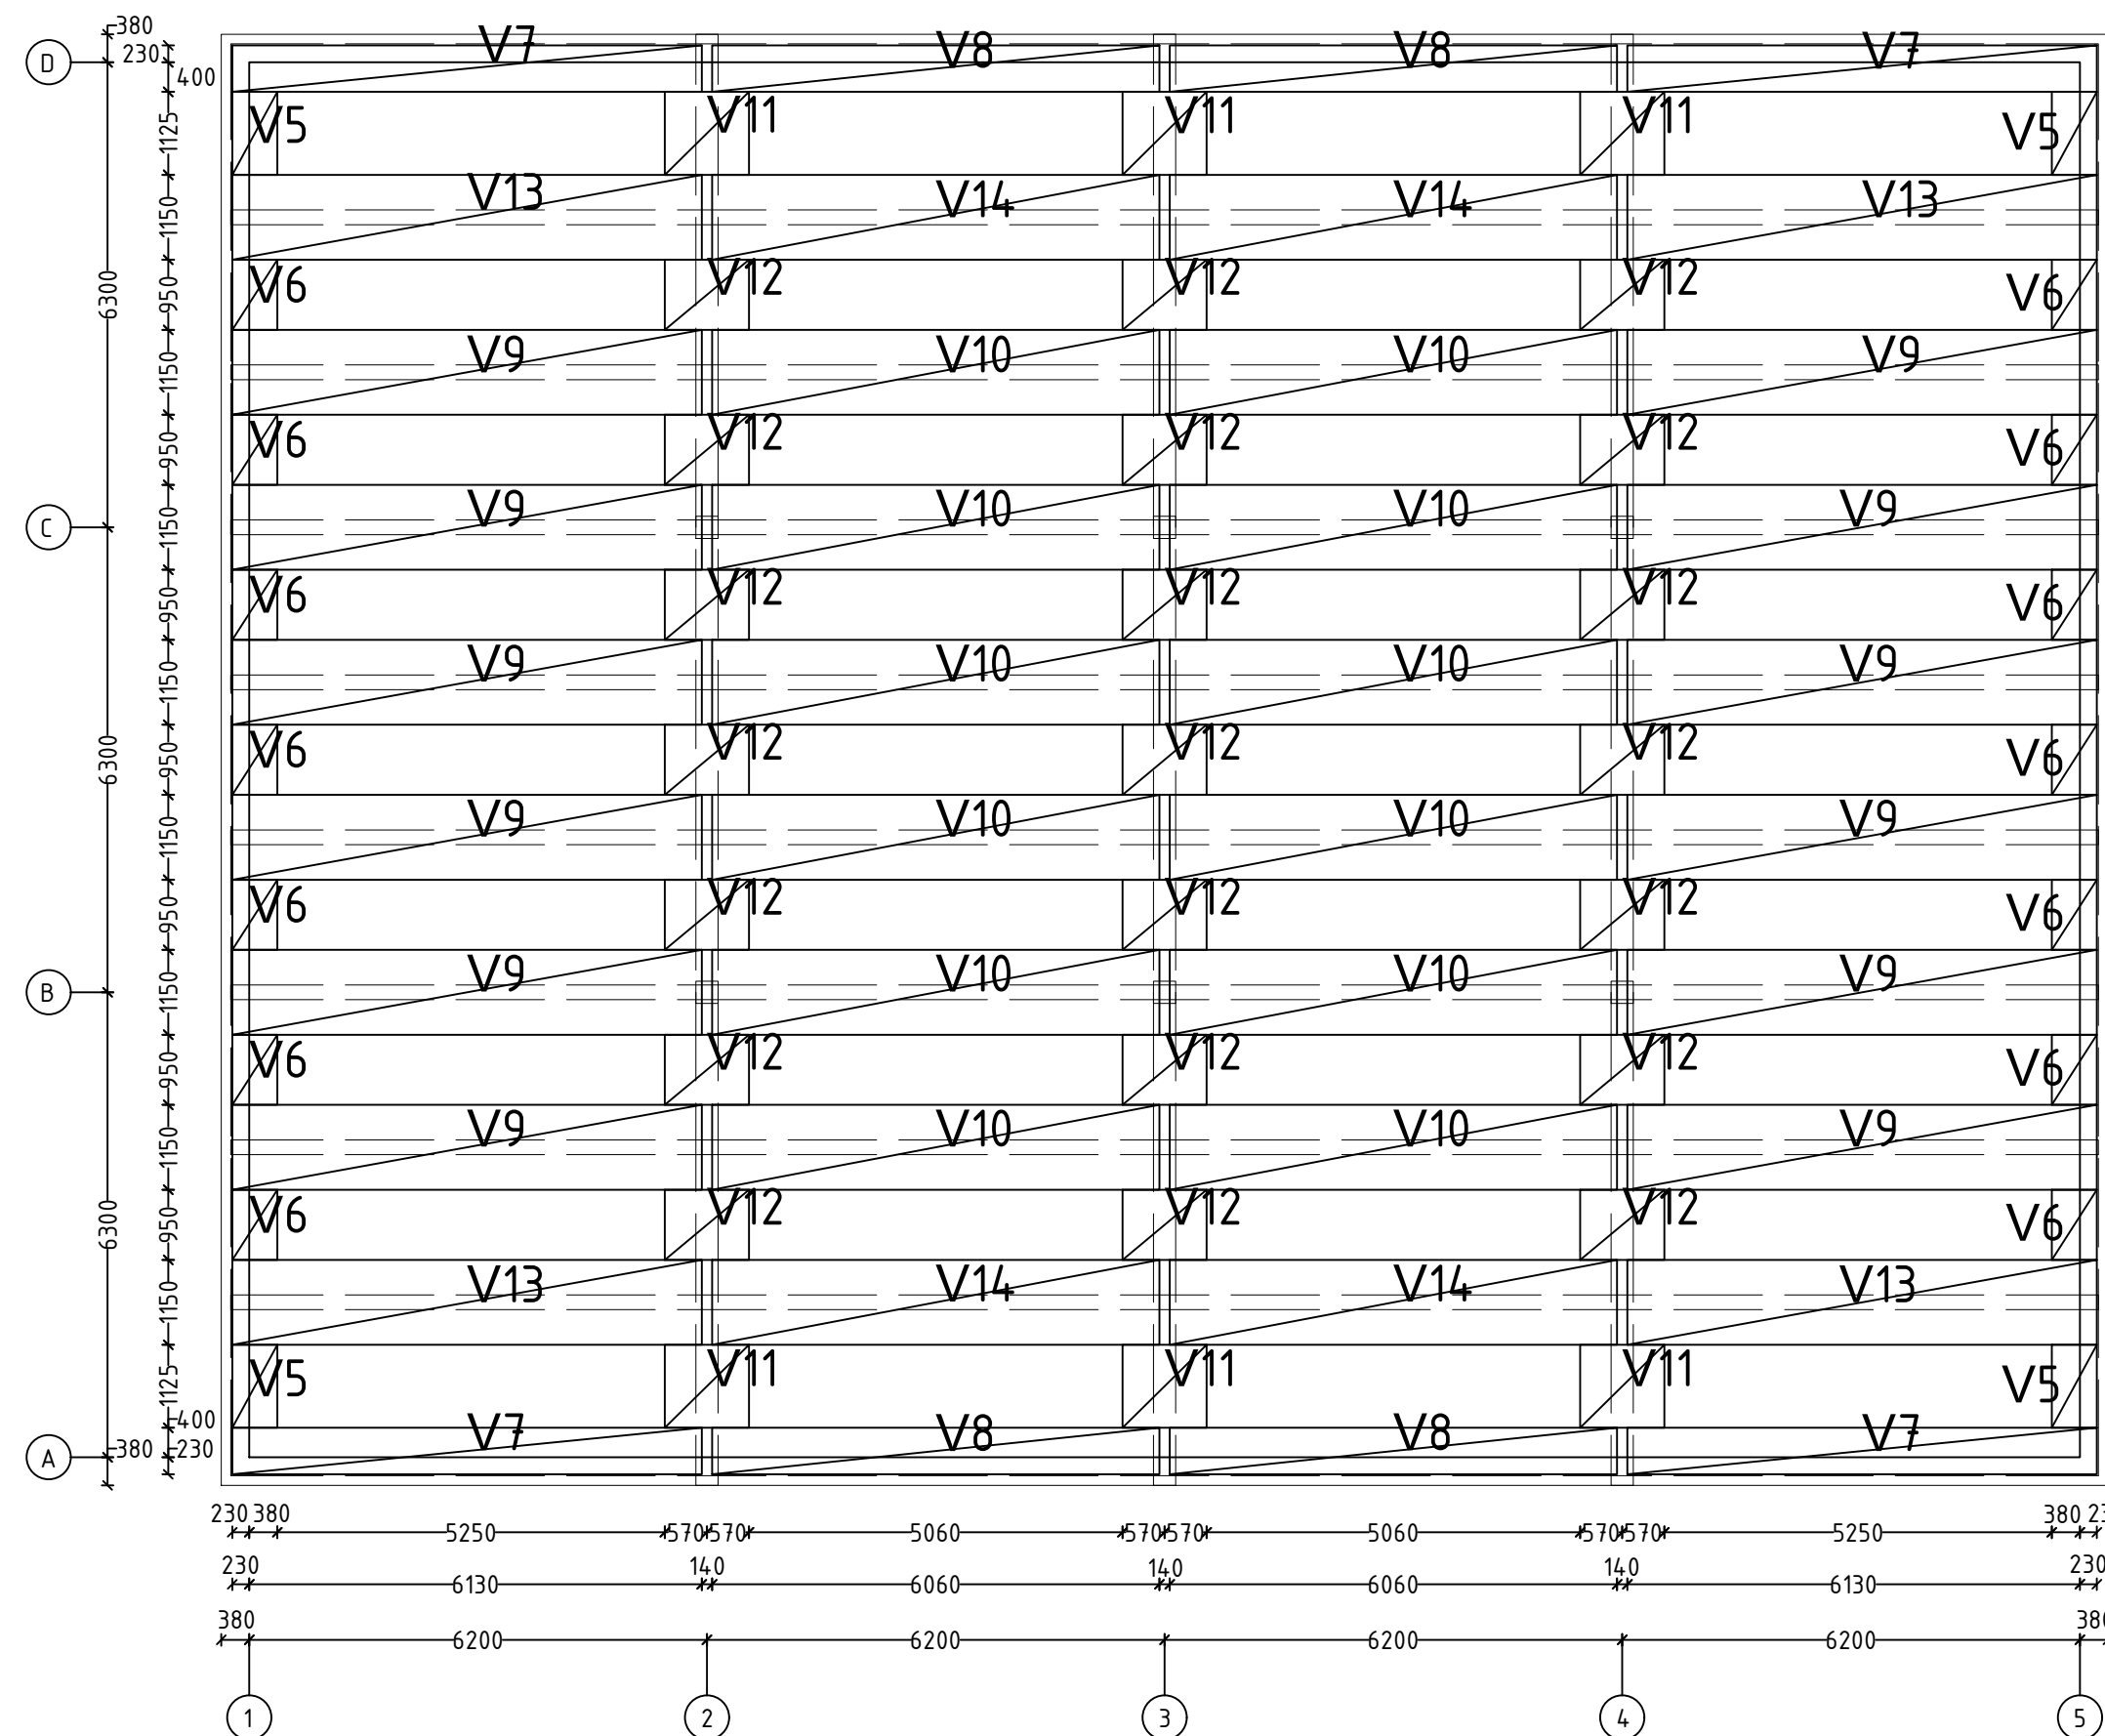

G-G 1:10

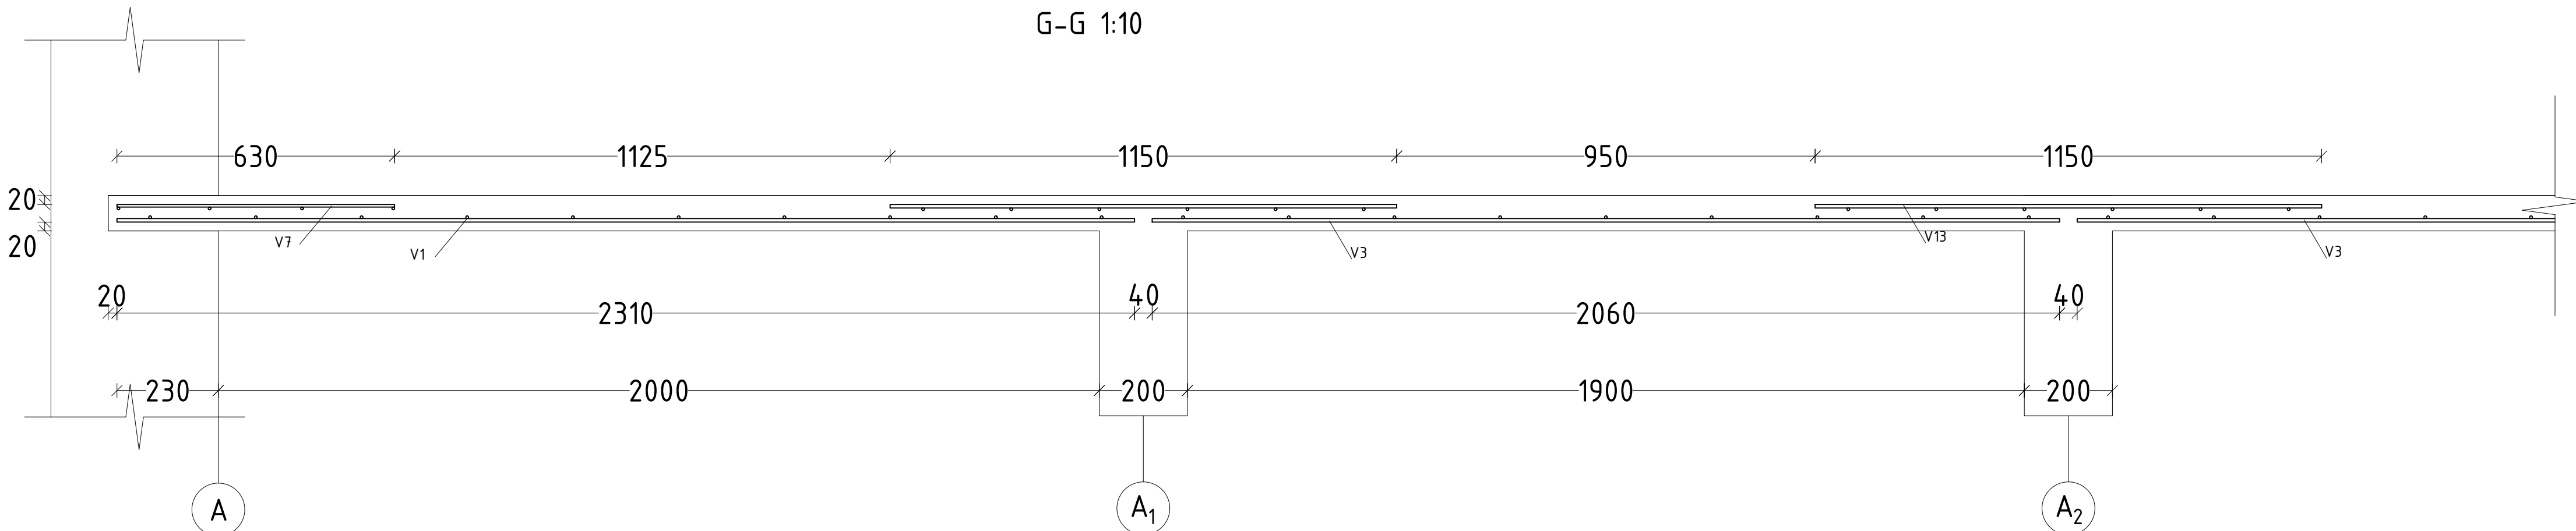

E-E 1:10

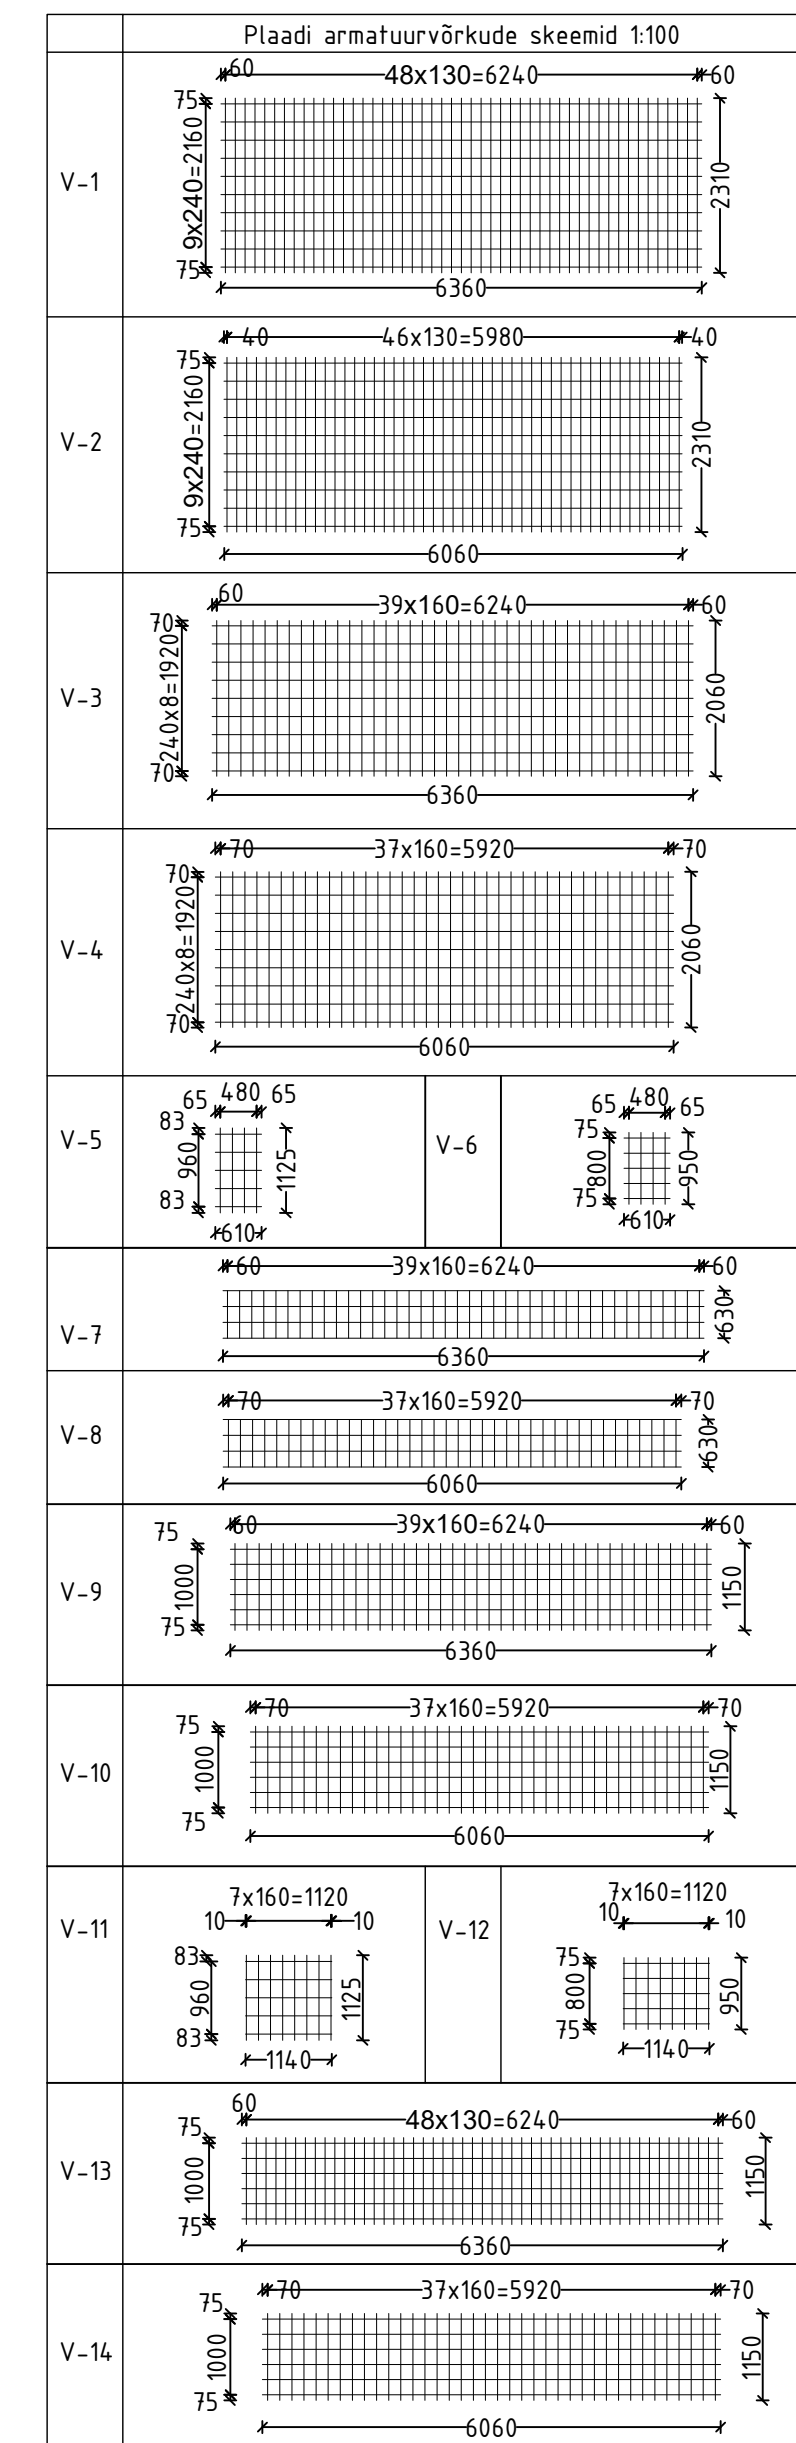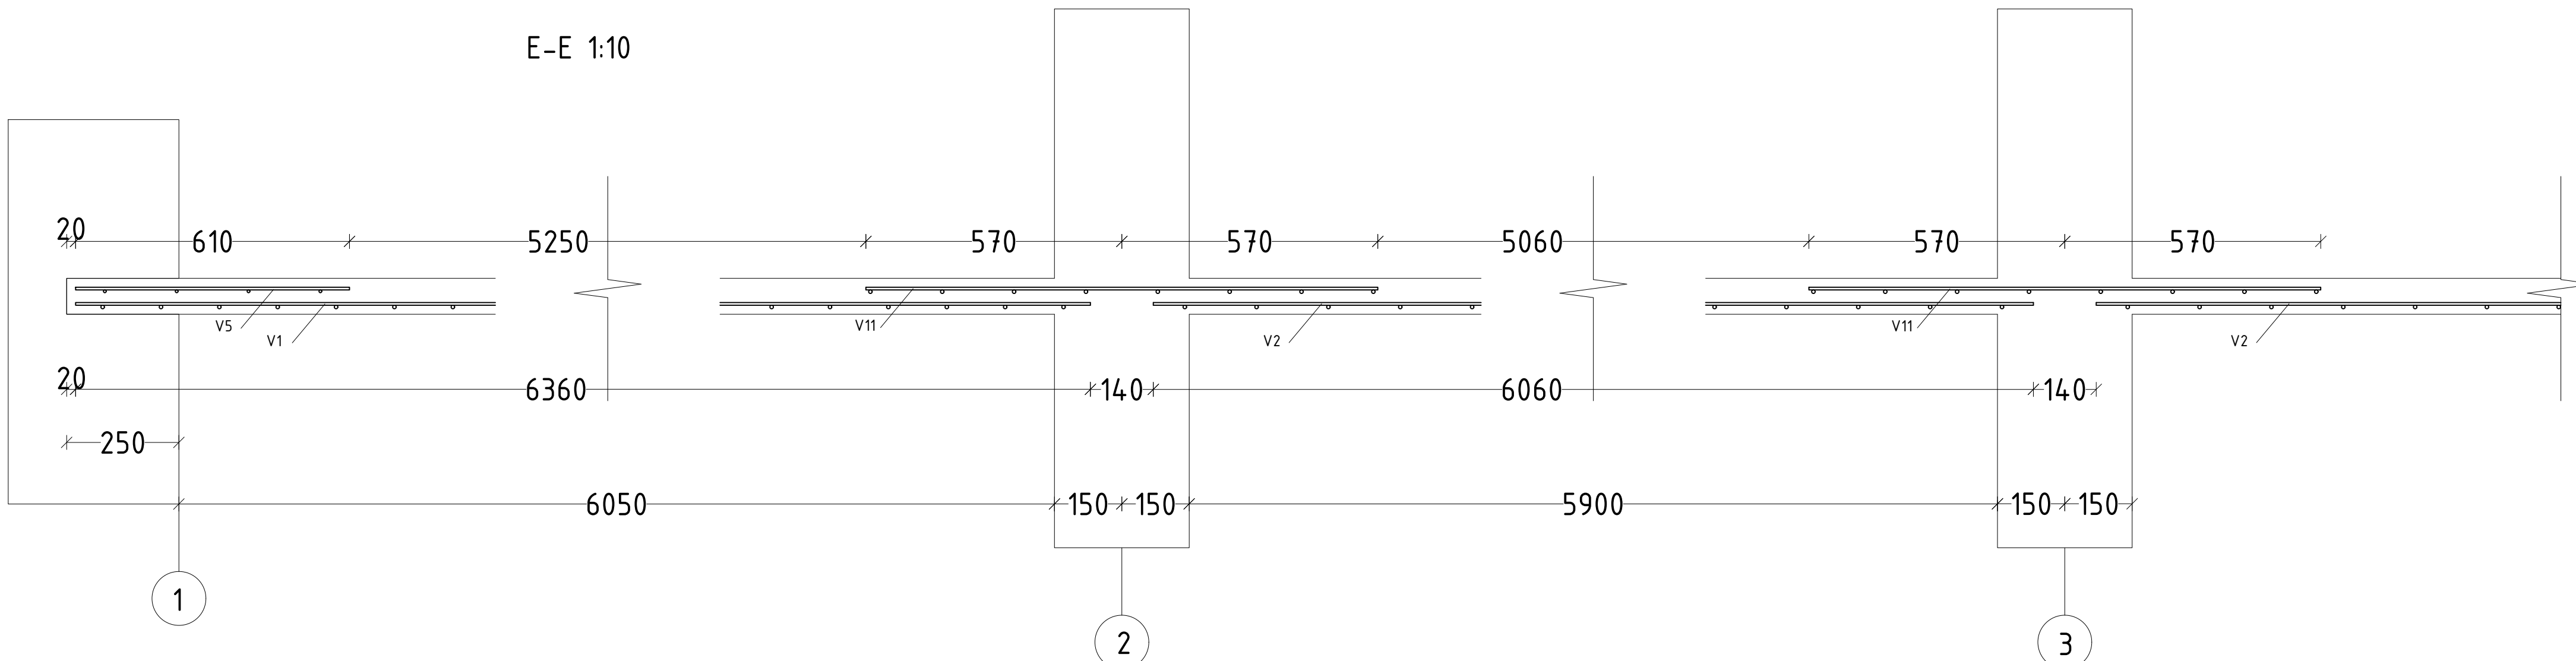

Plaadi armatuurvõrkude kokkuvõte				
Tähis	Armatuuri klass	Pikiarmatuuri kogus-läbimõõt-pikkus-samm, tk-mm-mm-mm-mm	Jaotusarmatuuri kogus-läbimõõt-pikkus-samm, tk-mm-mm-mm-mm	Võrgu kogus, tk
V-1	B500B	4-Ø8-L2310-S130	10-Ø6-L6360-S240	4
V-2	B500B	4-Ø8-L2310-S130	10-Ø6-L5980-S240	4
V-3	B500B	4-Ø8-L2060-S160	9-Ø6-L6360-S240	14
V-4	B500B	38-Ø8-L2060-S160	9-Ø6-L6060-S240	14
V-5	B500B	4-Ø8-L1125-S160	5-Ø6-L480-S240	4
V-6	B500B	4-Ø8-L950-S160	5-Ø6-L610-S240	14
V-7	B500B	4-Ø8-L630-S160	4-Ø6-L6360-S240	4
V-8	B500B	38-Ø8-L630-S160	4-Ø6-L6060-S240	4
V-9	B500B	4-Ø8-L1150-S160	6-Ø6-L6360-S200	12
V-10	B500B	38-Ø8-L1150-S160	6-Ø6-L6060-S200	12
V-11	B500B	8-Ø8-L1125-S160	5-Ø6-L1140-S240	6
V-12	B500B	8-Ø8-L1950-S160	5-Ø6-L5980-S200	21
V-13	B500B	4-Ø8-L1150-S160	6-Ø6-L6360-S200	4
V-14	B500B	38-Ø8-L1150-S160	6-Ø6-L6060-S200	4

Technical drawing of a bridge deck cross-section showing reinforcement details. The drawing includes a top view of the bridge deck with reinforcement bars (4x32, 2x28, 2x32, 3x32) and a bottom view showing the reinforcement layout (Armatuur ülemises pinnas and Armatuur alumises pinnas). The drawing is divided into sections A, B, C, and D. The top view shows the bridge deck with reinforcement bars and dimensions. The bottom view shows the reinforcement layout with dimensions and reinforcement bar specifications.

Top View Details:

- Reinforcement bars: 4x32 606.4, 2x28 237, 2x32 377, 3x32 563.
- Dimensions: 532.5, 431, 319.93, 215, 265.9, 574.7.
- Section labels: A, B, C, D.

Bottom View Details:


- Reinforcement bars: 4x32 606.4, 2x28 237, 2x32 377, 3x32 563.
- Dimensions: 532.5, 431, 319.93, 215, 265.9, 574.7.
- Section labels: A, B, C, D.




Reinforcement Layout (Armatuur ülemises pinnas):

- Reinforcement bars: 4x32 606.4, 2x28 237, 2x32 377, 3x32 563.
- Dimensions: 532.5, 431, 319.93, 215, 265.9, 574.7.
- Section labels: A, B, C, D.








Reinforcement Layout (Armatuur alumises pinnas):

- Reinforcement bars: 4x32 606.4, 2x28 237, 2x32 377, 3x32 563.
- Dimensions: 532.5, 431, 319.93, 215, 265.9, 574.7.
- Section labels: A, B, C, D.

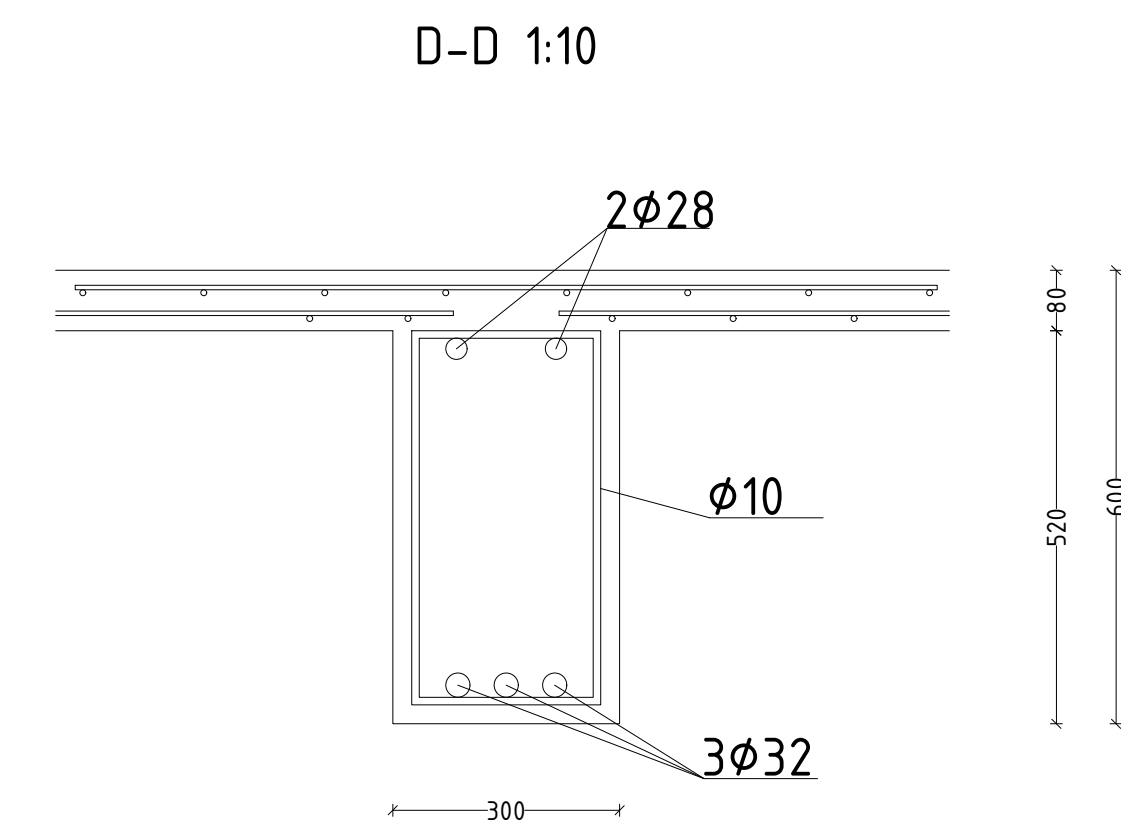

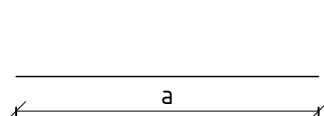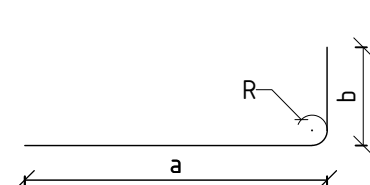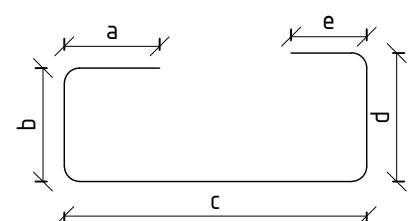Peatala armatuuri kokkuvõte																			
Element	Pos	Armatuuri klass	Ø,mm	Pikkus, mm	Elementide arv, tk	Arv vahelase kokku, tk	Kuju kood			Haak	Painutusmõõdud, mm								
											a	b	c	d	e	R			
Peatala	1	B500B	32	4755	8	24	00	0	0	4755									
Peatala	2	B500B	32	5500	6	18	00	0	0	5500									
Peatala	3	B500B	32	7000	2	6	00	0	0	7000									
Peatala	4	B500B	32	5510	2	6	00	0	0	5510									
Peatala	5	B500B	28	5500	4	12	00	0	0	5500									
Peatala	6	B500B	28	4300	2	6	00	0	0	4300									
Peatala	7	B500B	20	1385,7	4	12	12	0	0	1250	190					70			
Peatala	8	B500B	10	1450	110	330	41	0	0	100	240	485	240	385					
  																			
00	0	0	a		12	0	0	a	b	R		41	0	0	a	b	c	d	e

POSTI JA VUNDAMENDI ARMEERIMINE
1:50

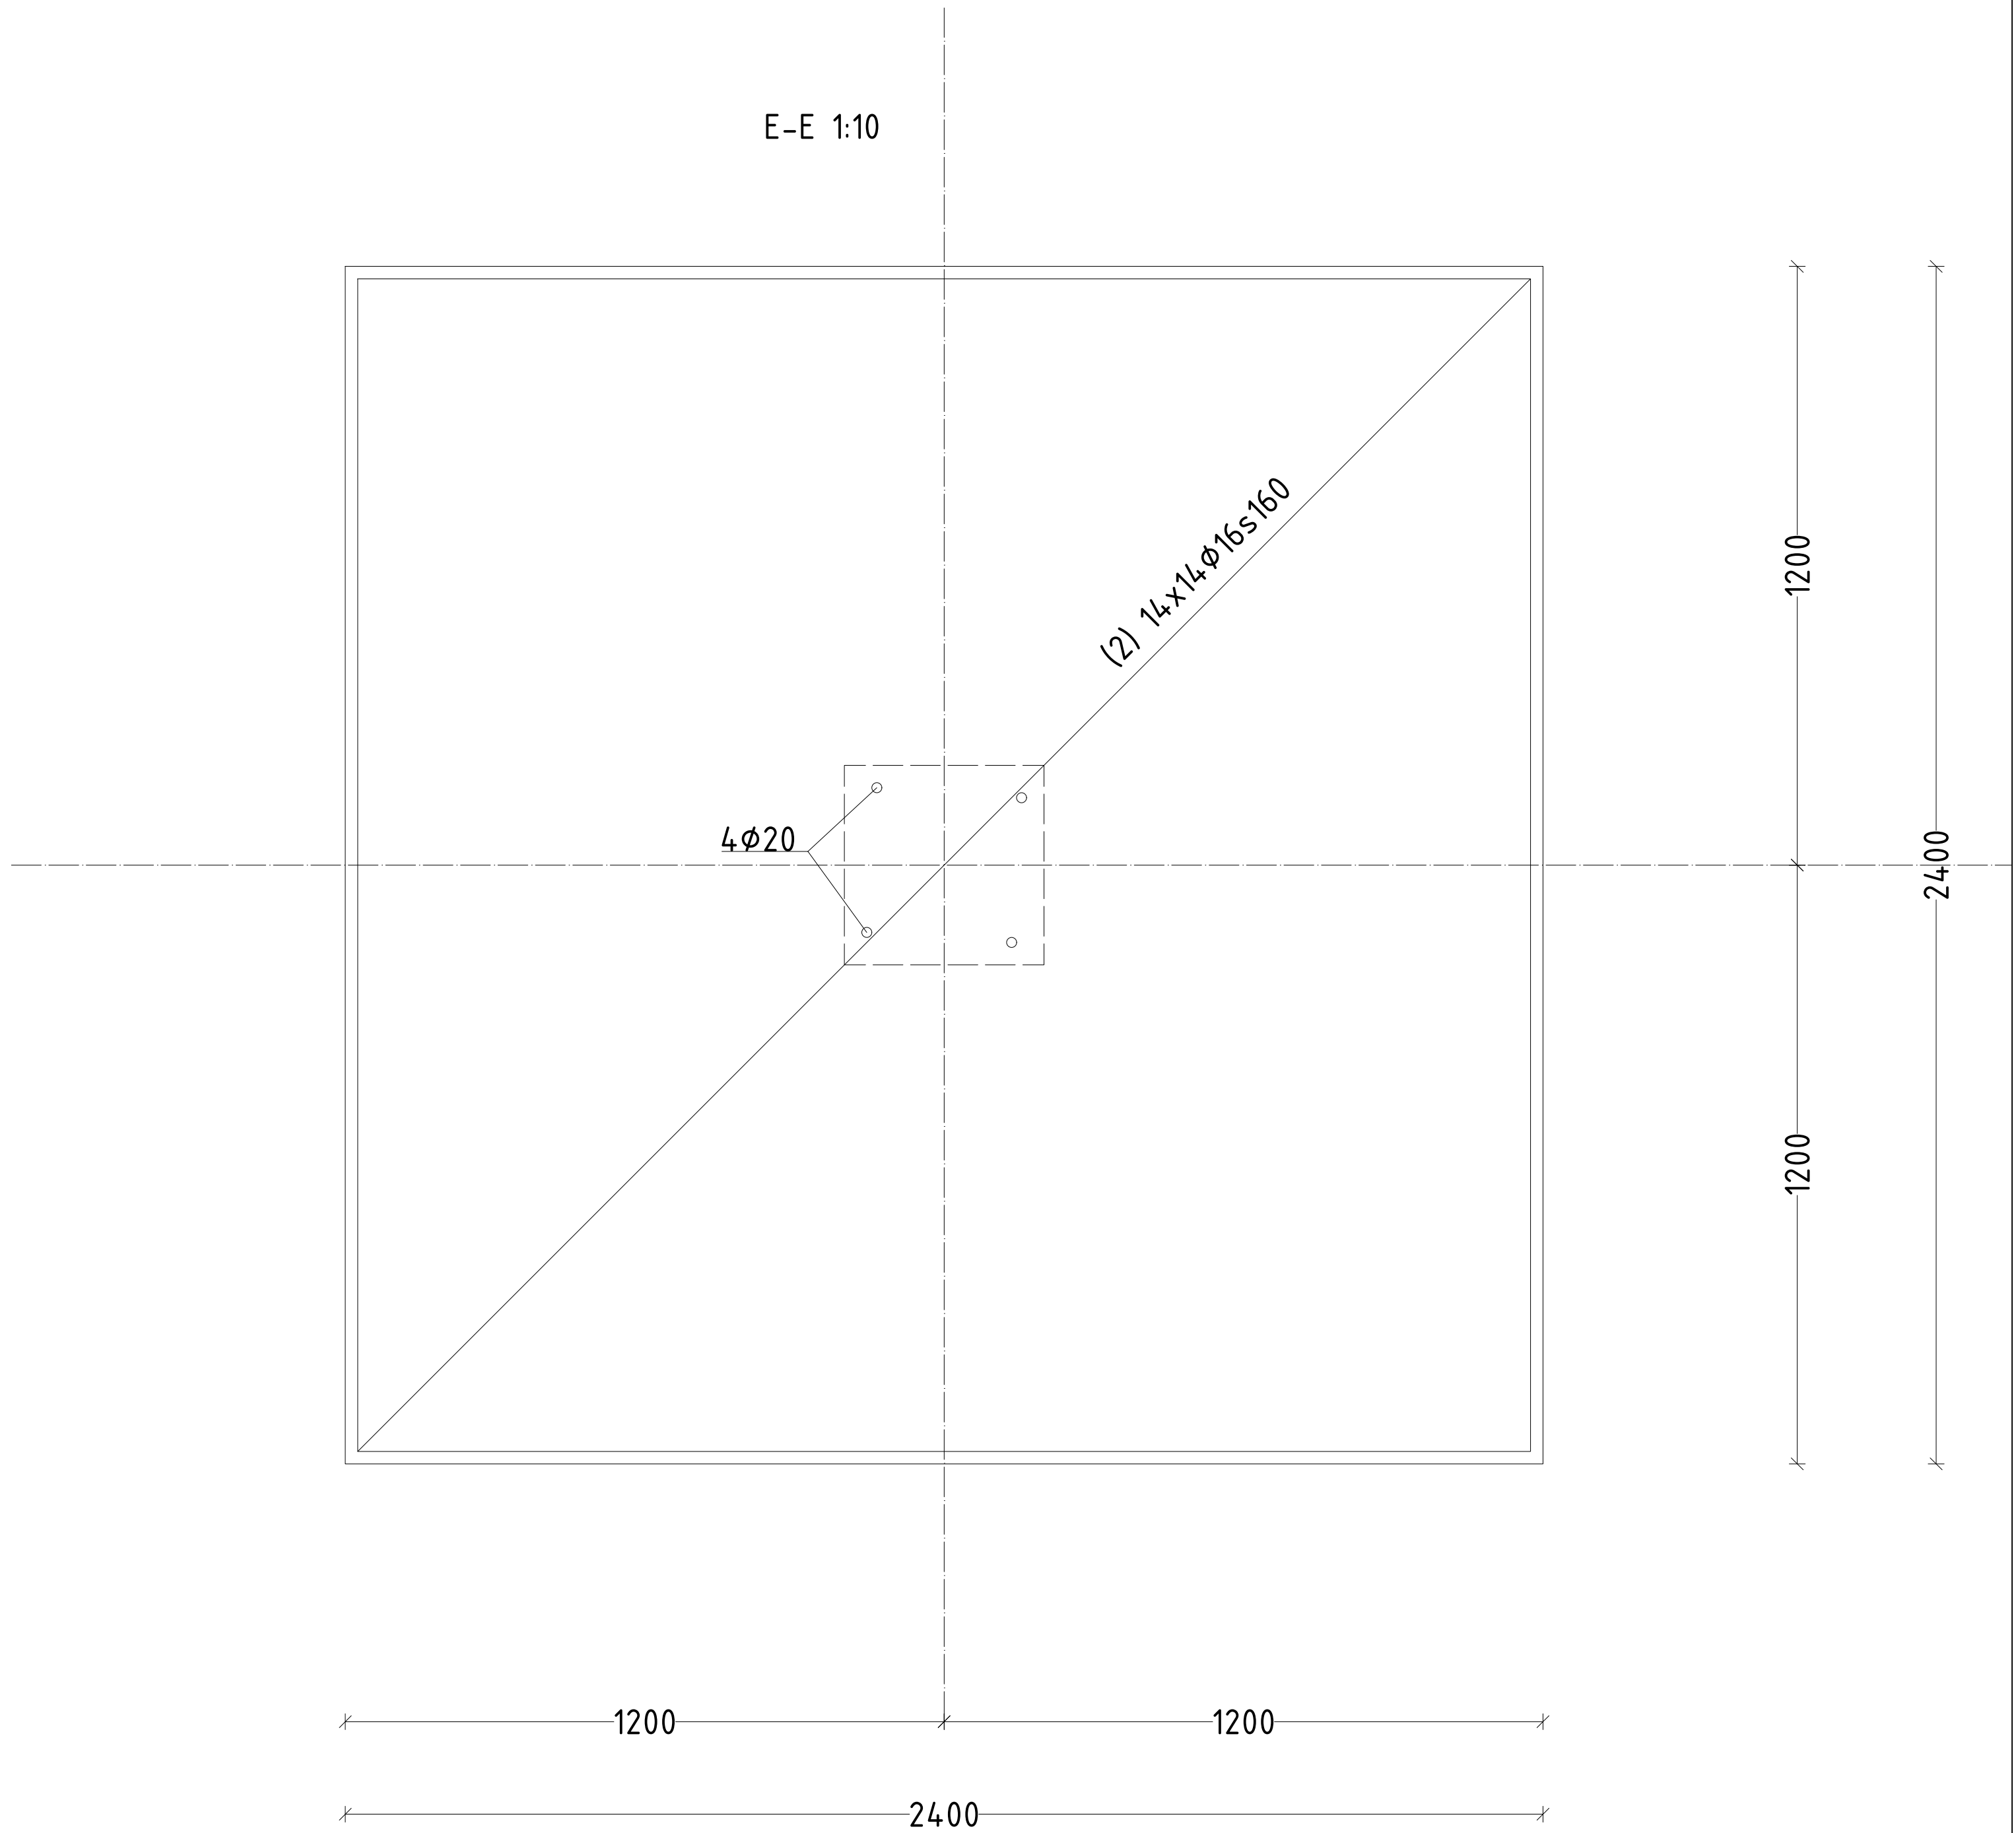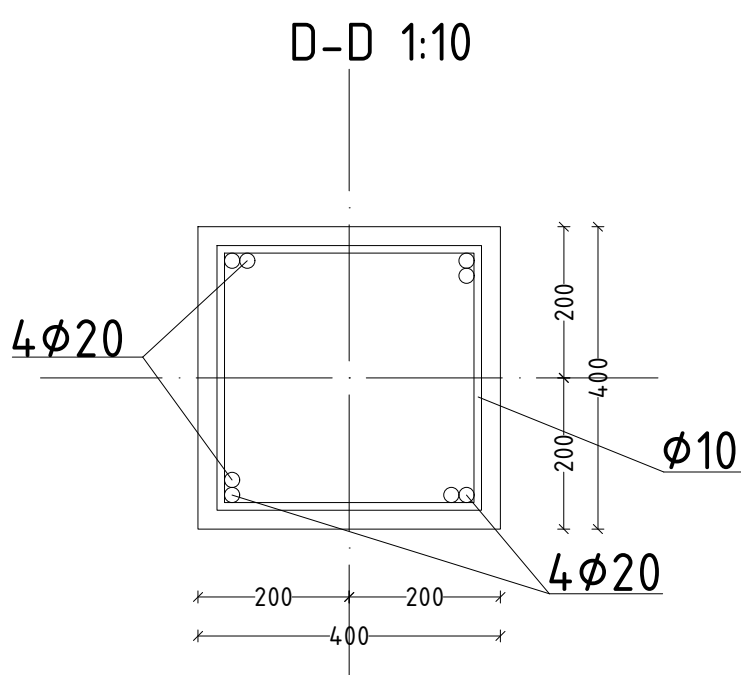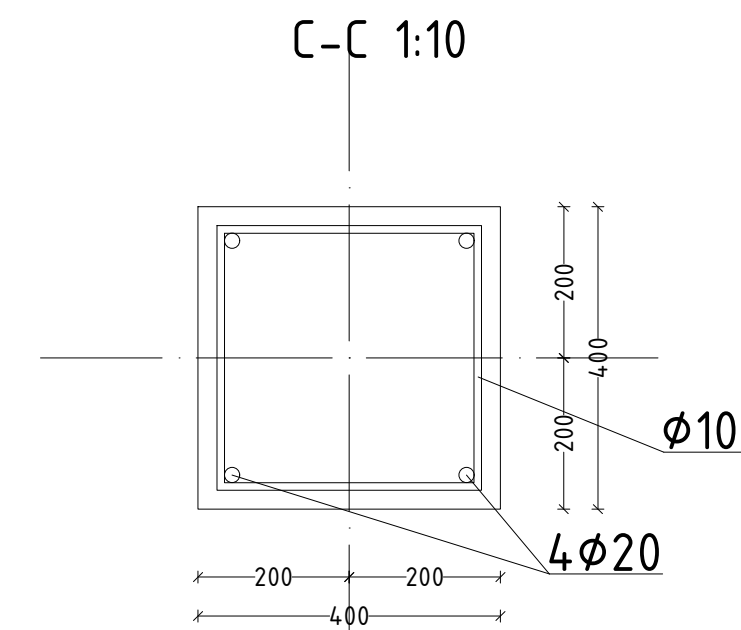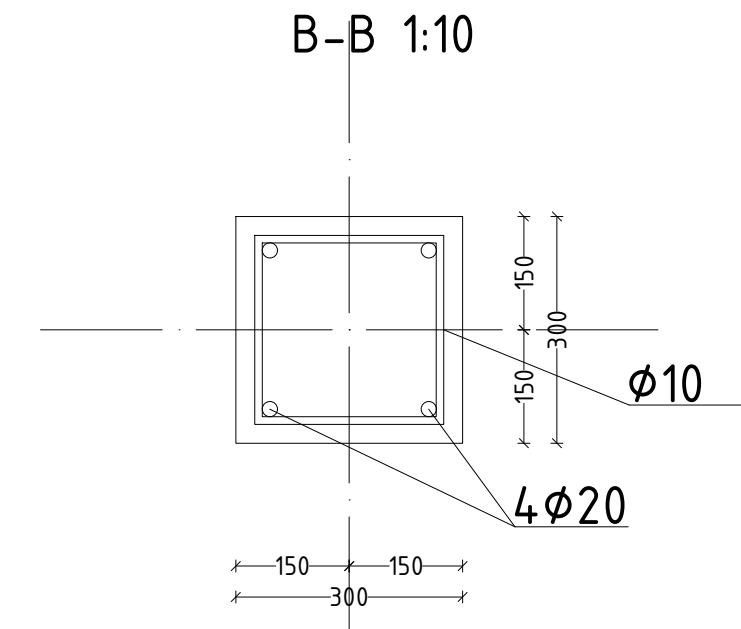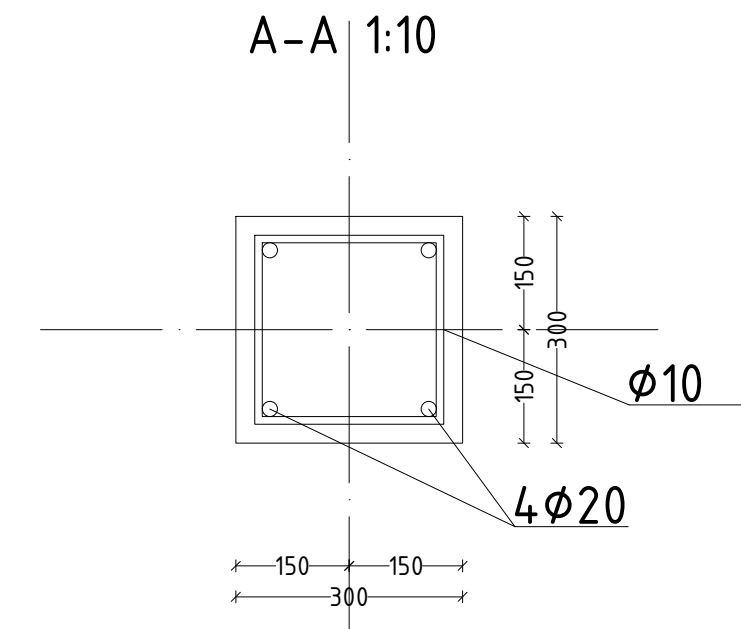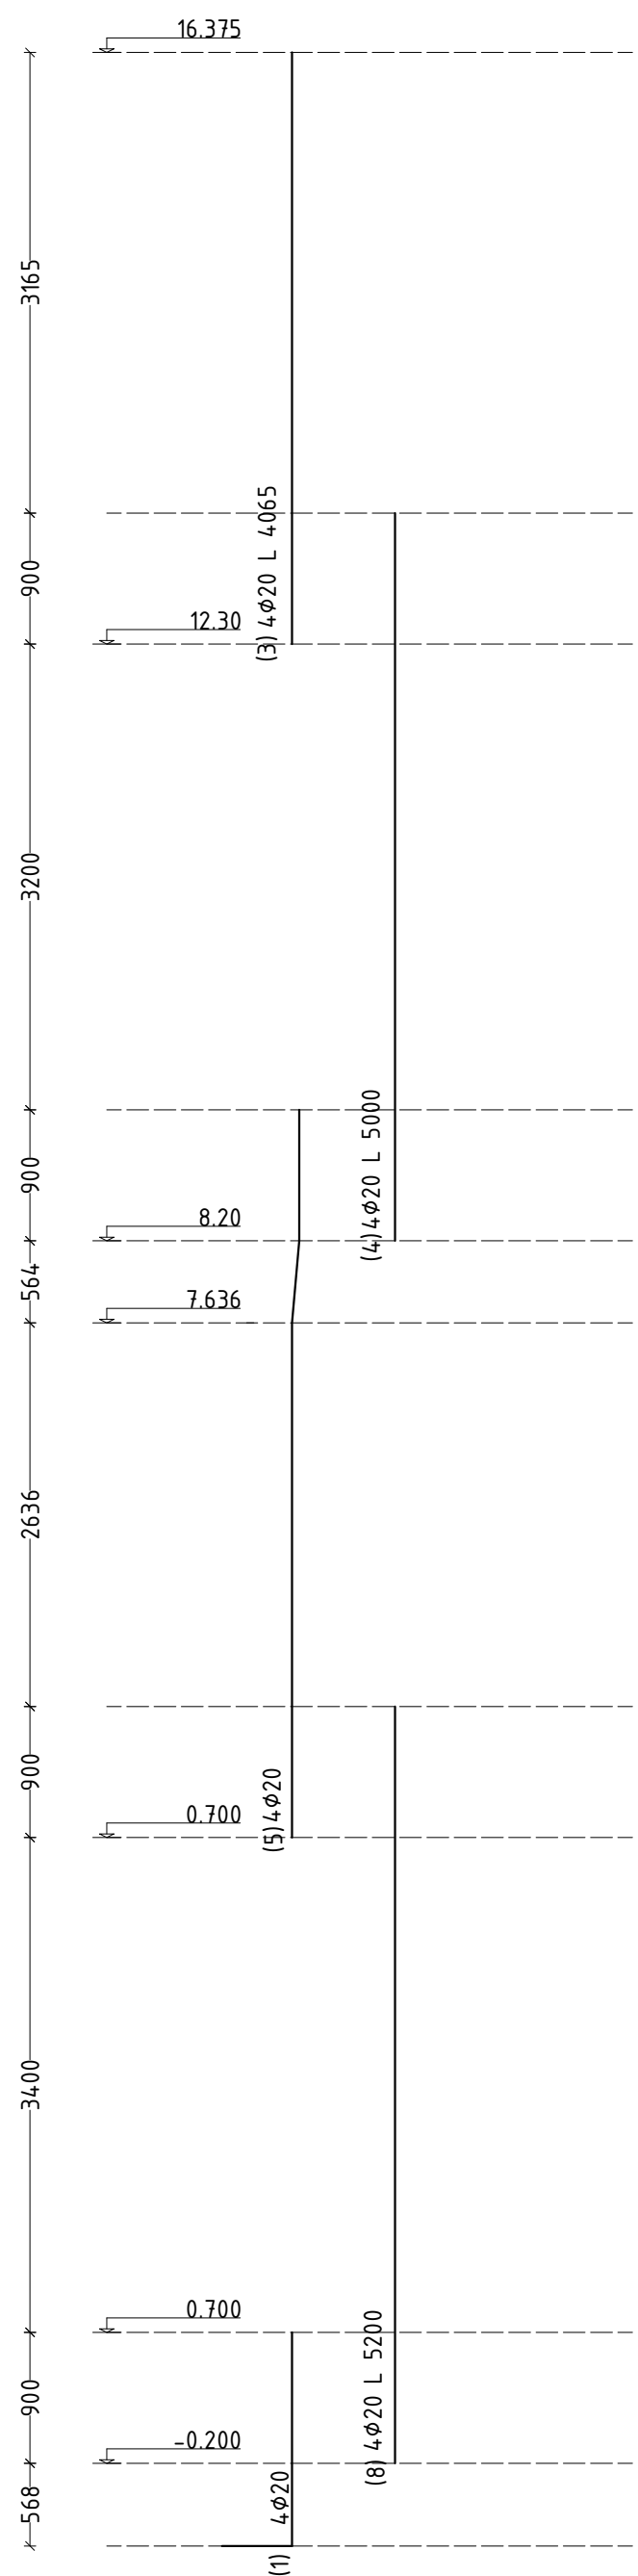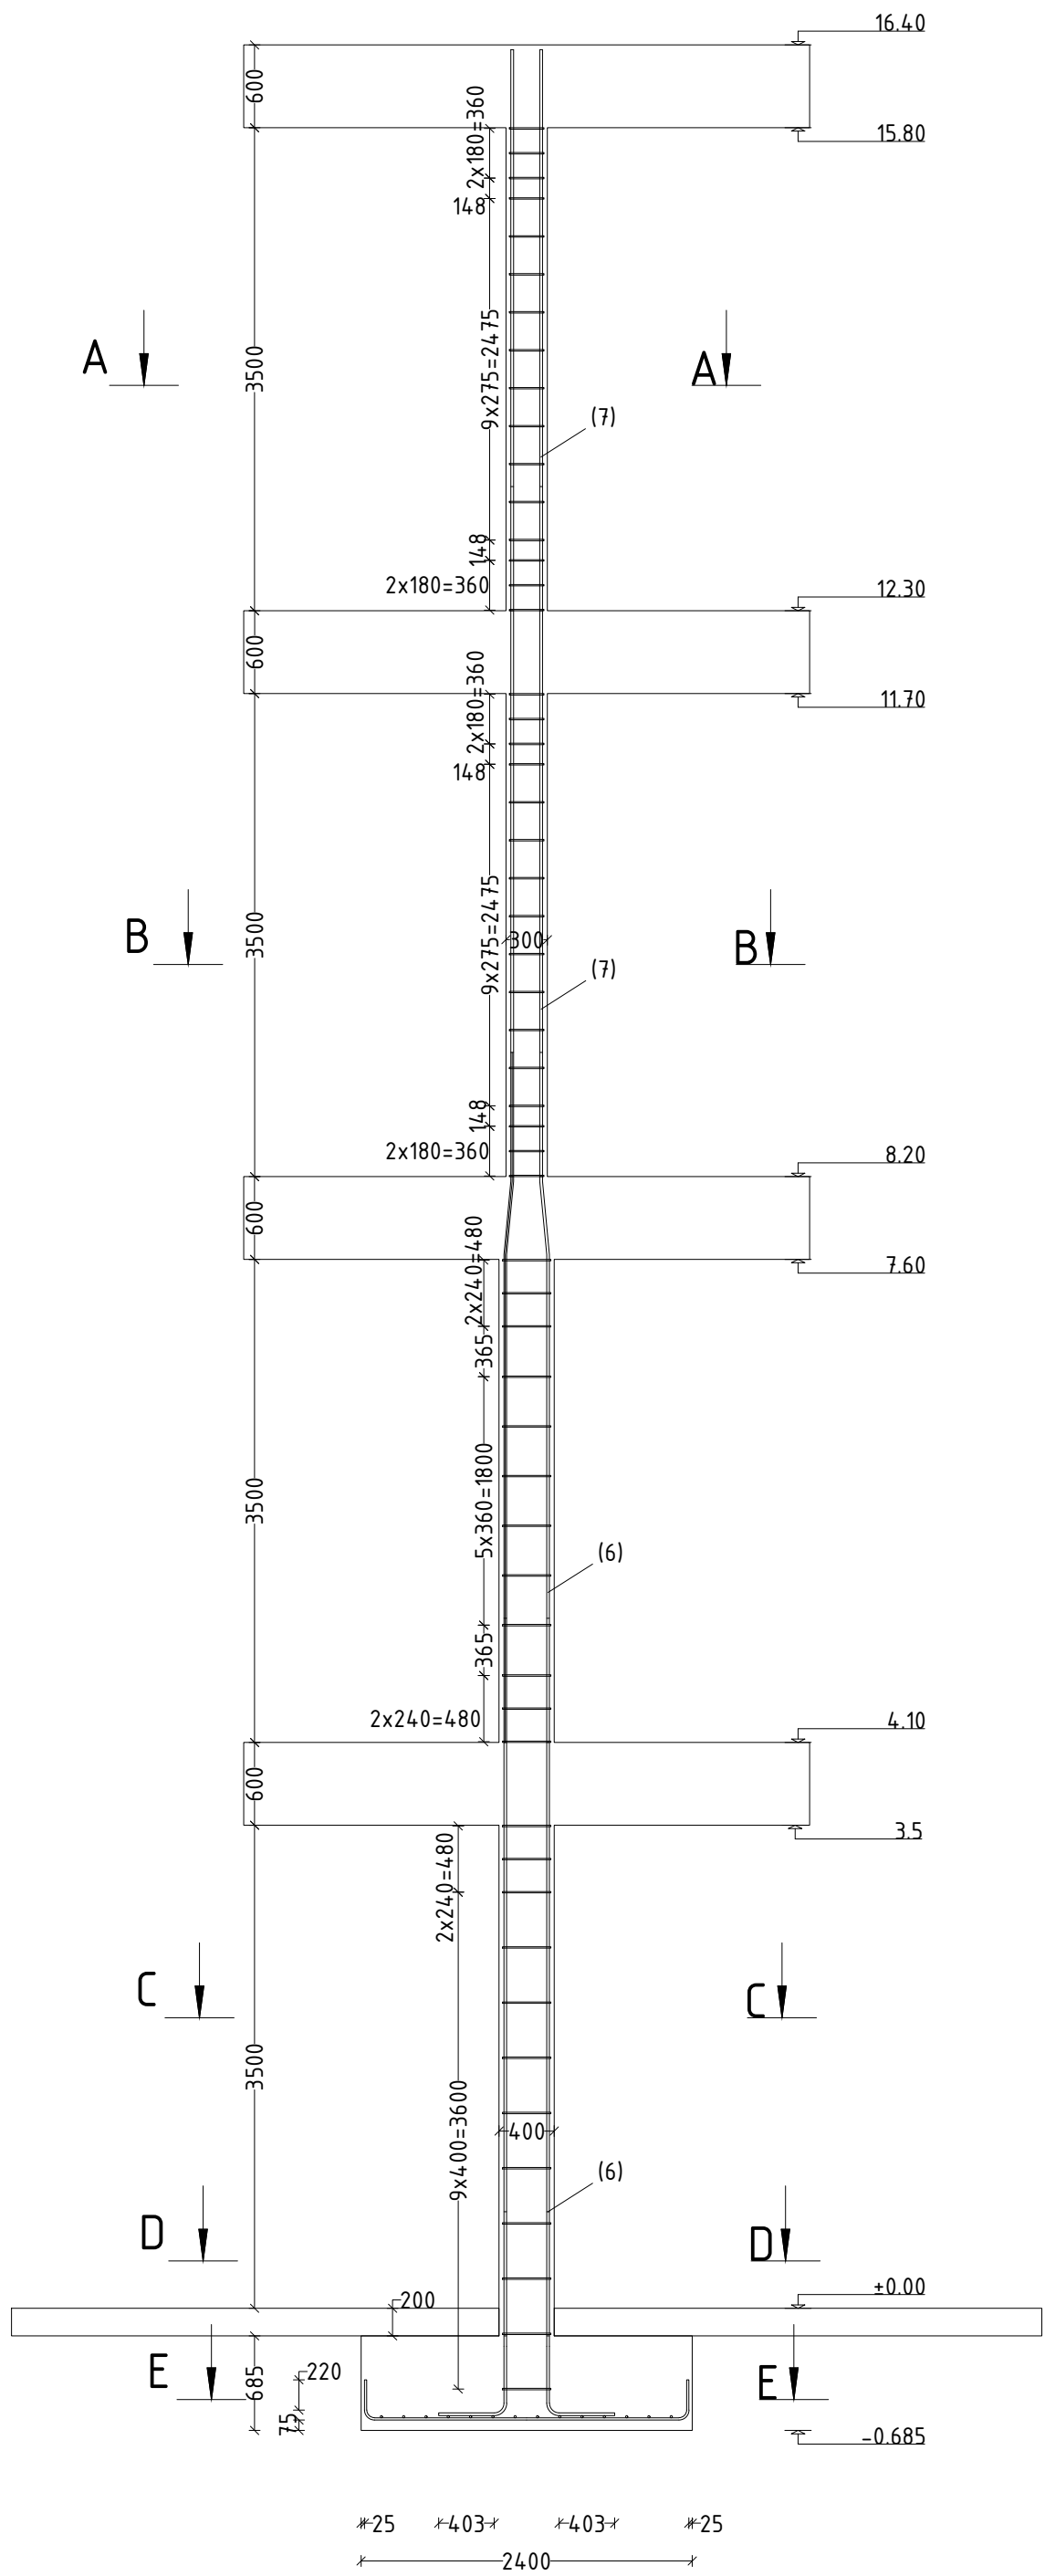

	Armatuuri kokkuvõte														
Element	Pos	Armatuuri klass	Ø,mm	Pikkus, mm	Elementide arv, tk	Arv kokku, tk	Kuju kood	Haak	Painutusmõõdud, mm						
									a	b	c	d	e	R	
Vundament	1	B500B	20	1917	4	24	12	0	0	1388	483				70
Vundament	2	B500B	16	2848	28	168	21	0	0	284	2334	284			
Post	3	B500B	20	4065	4	24	00	0	0	4065					
Post	4	B500B	20	5000	4	24	00	0	0	5000					
Post	5	B500B	20	5000	4	24	26	0	0	3535	530	935	50		
Post	6	B500B	10	1360	24	144	41	0	0	170	340	340	340	170	
Post	7	B500B	10	960	32	192	41	0	0	120	240	240	240	120	
Post	8	B500B	20	5200	4	24	00	0	0	5200					

